

Flanged bearing plate

ORTHOGRAPHIC DRAWING / STEPPED BORE AND FOUR-POINT MOUNT

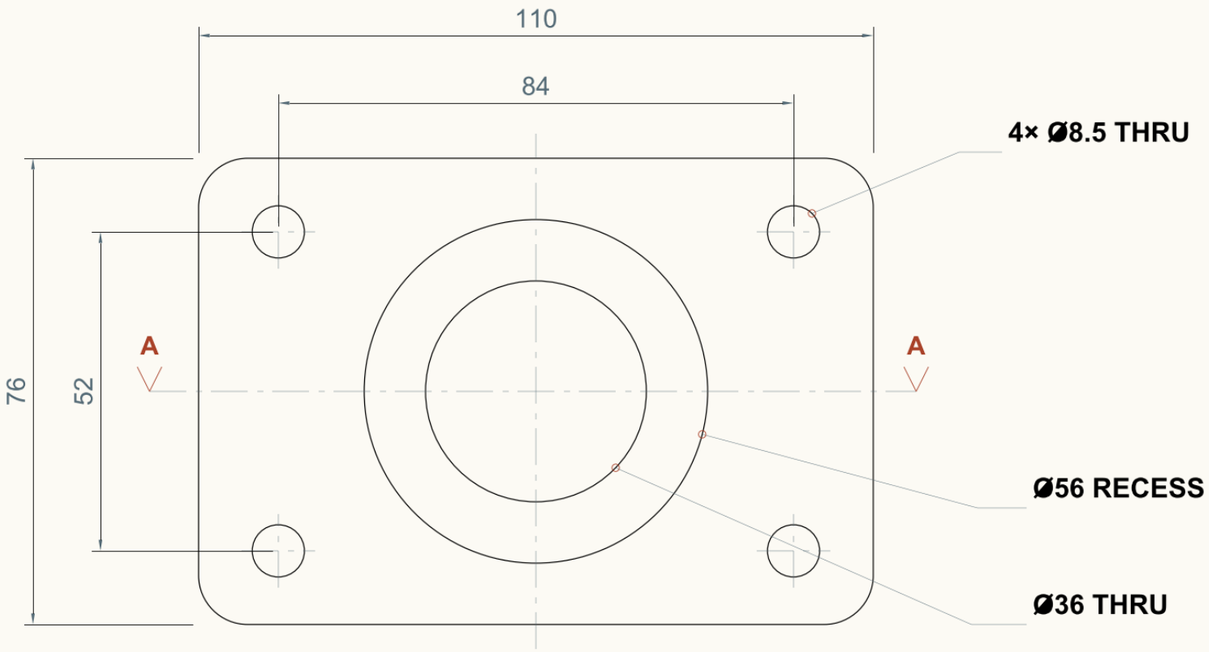


01 TOP VIEW

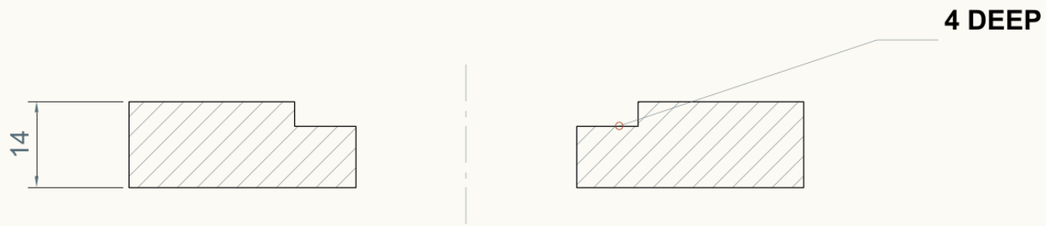

02 SECTION A–A

03 ISOMETRIC / NTS

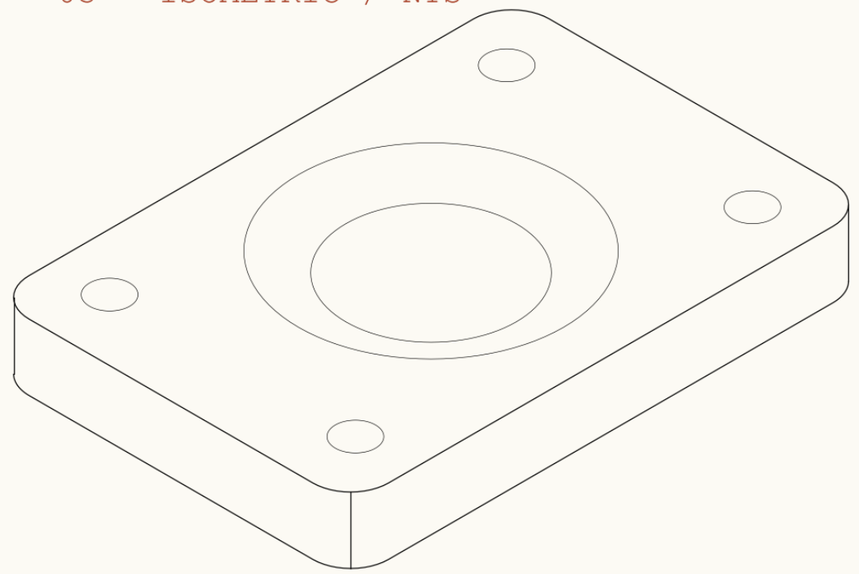


DESIGN DATA

Envelope	**110 × 76 × 14 mm**
External corners	**4 × R8**
Mount pattern	**84 × 52 mm, centered**
Bore	**Centered on plate**
Material intent	**6061 aluminum**

Courtyard studio

ONE-BEDROOM CONCEPT / DAYLIGHT, STORAGE AND AN OPEN LIVING EDGE

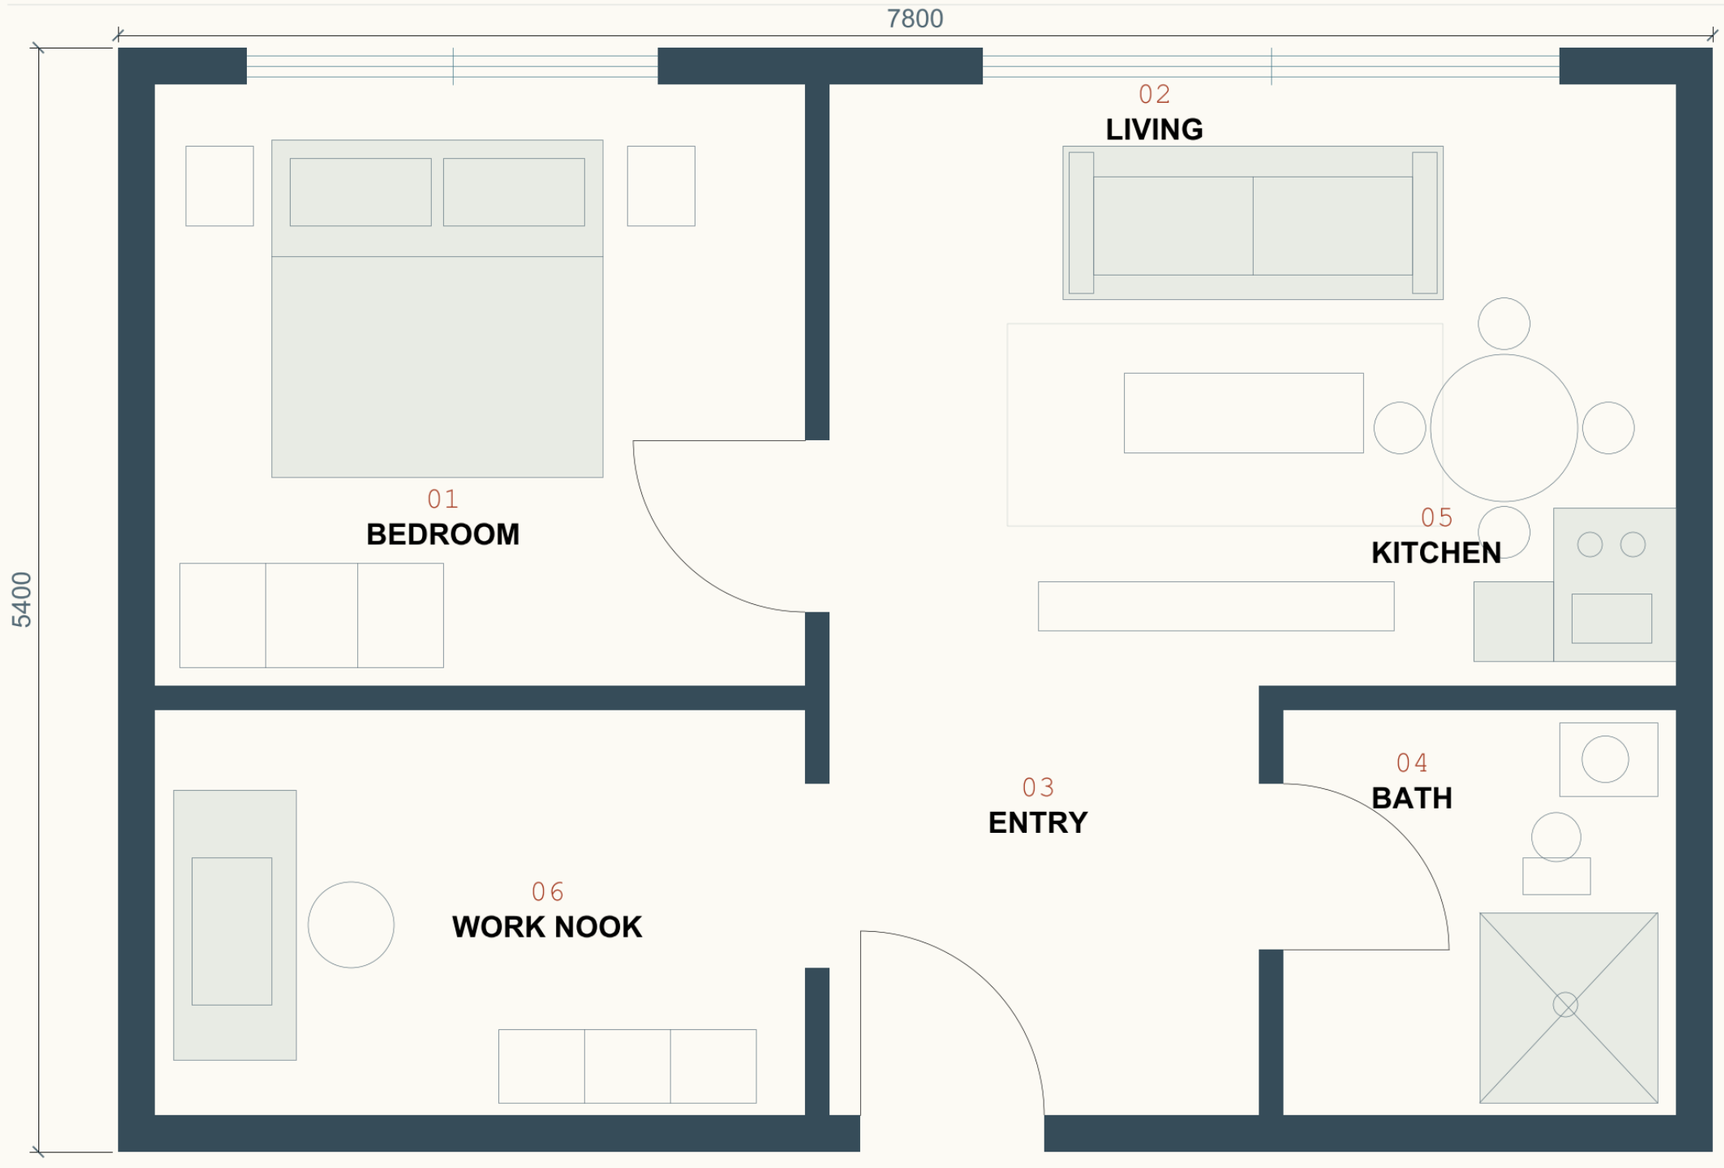

01 FURNISHED FLOOR PLAN

01 / FOOTPRINT

42.12 m² gross

7.80 × 5.40 m to outside face. North glazing serves the bedroom and the main living space.


02 / ORGANIZATION

Compact wet core

Kitchen and bath share a wall. The entry opens into a central route through the apartment.


03 / SCALE

North + scale bar

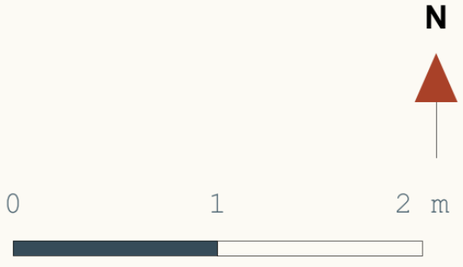

Dual status indicator

LOW-VOLTAGE SCHEMATIC / TWO INDEPENDENT SWITCHED LED CHANNELS

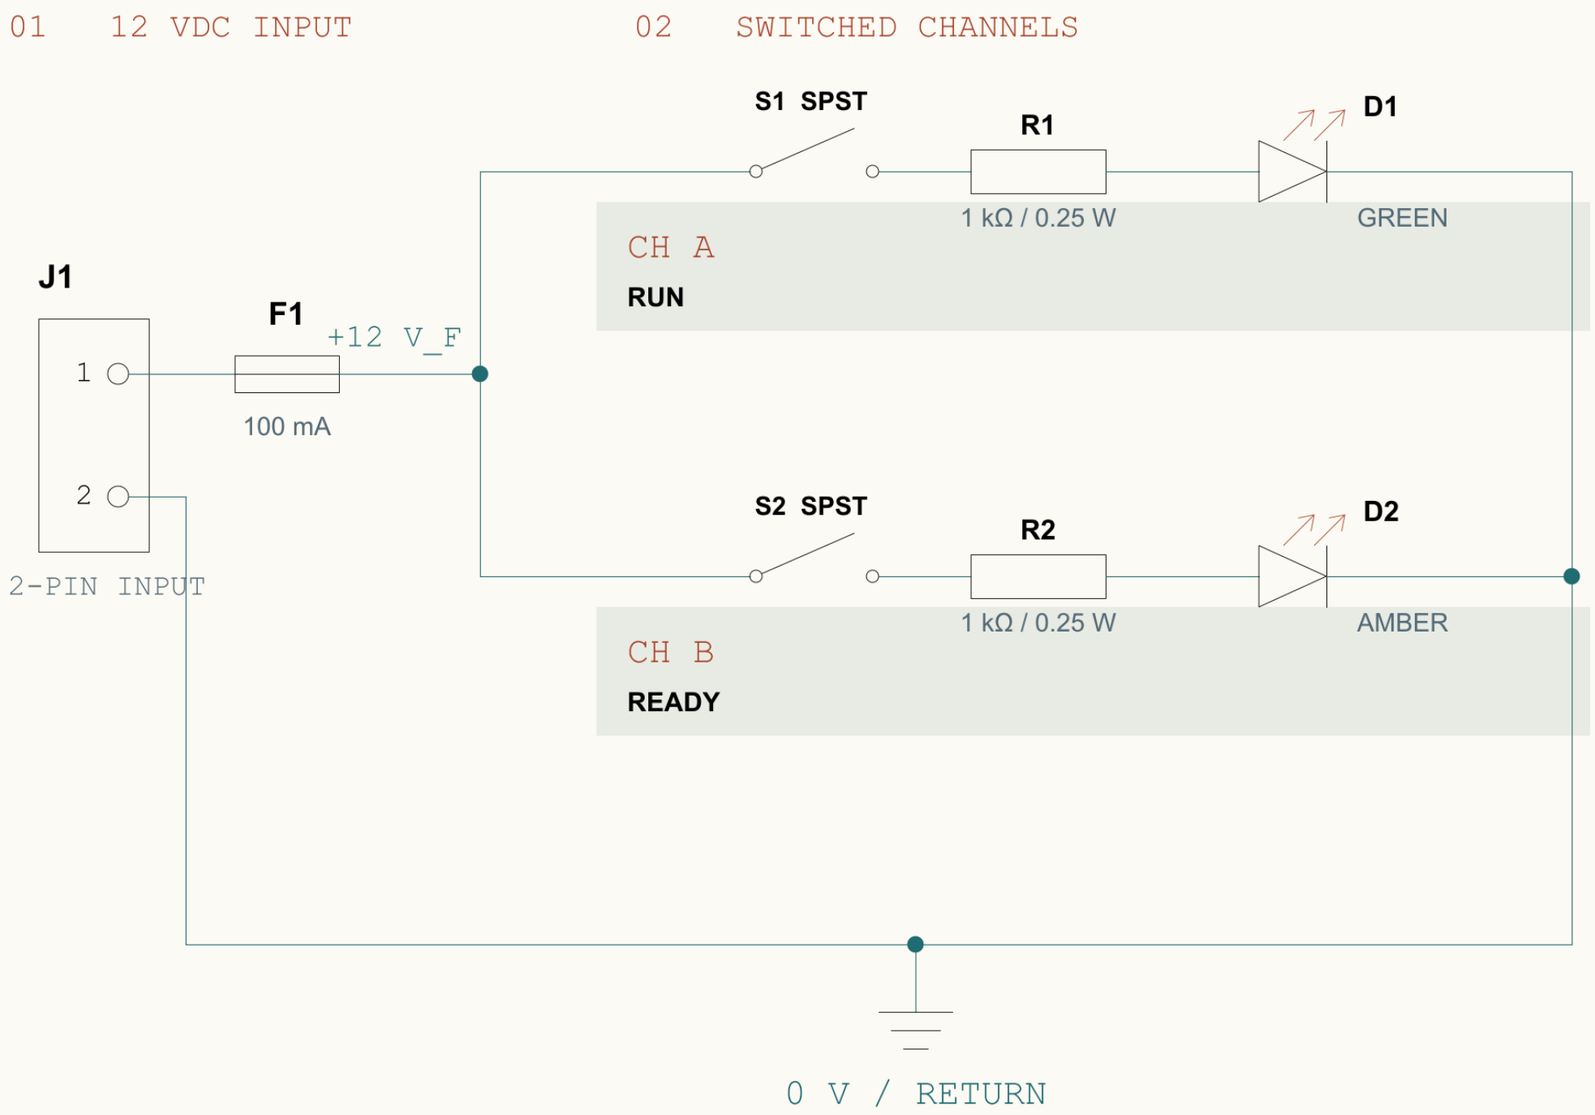

01 / SUPPLY

12 V DC input

J1 pin 1 feeds the fused rail.
J1 pin 2 is the common return.

02 / CHANNELS

Independent control

S1 enables the green RUN LED.
S2 enables the amber READY LED.
Each branch has its own resistor.


03 / CURRENT

≈ 10 mA per LED


At 12 V with 2.0 V forward drop.
Resistor dissipation ≈ 0.10 W.

Guide roller assembly


PLAIN-BEARING ROLLER / LONGITUDINAL SECTION, END VIEW AND RETENTION DETAIL

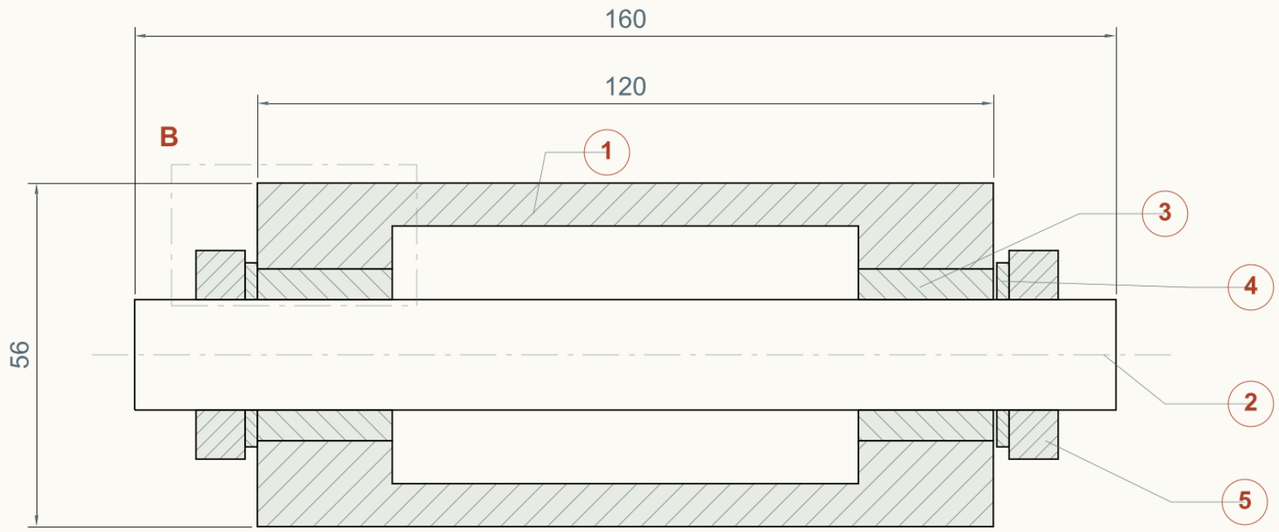

01 SECTION A-A

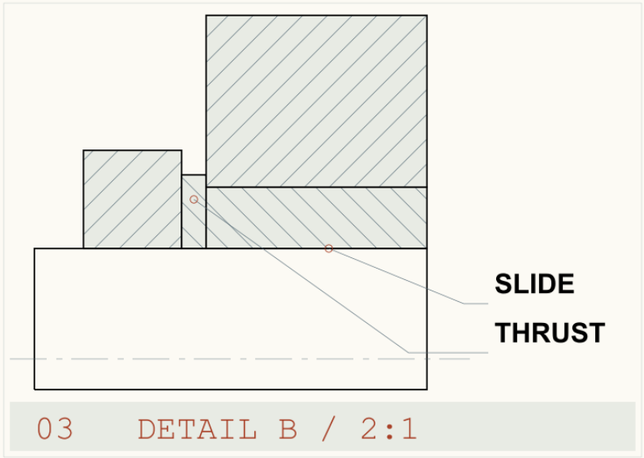

03 DETAIL B / 2:1

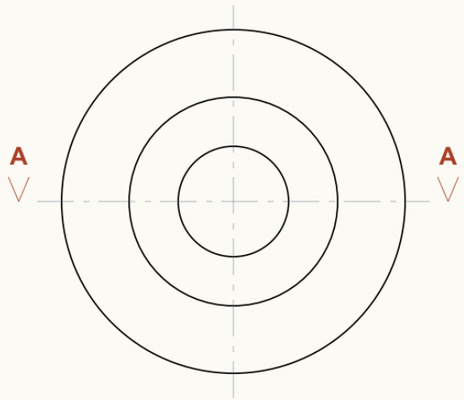

02 END VIEW

BOM / ASSEMBLY 04

NO	COMPONENT	QTY	MATERIAL INTENT
01	Stepped roller shell	1	6061 aluminum
02	Stationary shaft	1	Carbon steel
03	Sleeve bushing	2	Bearing bronze
04	Thrust washer	2	PTFE composite
05	Clamp collar	2	Carbon steel


INTERFACE / NOMINAL

FEATURE	SIZE / LOCATION
Roller shell	Ø56 × 120 mm
Shaft	Ø18 × 160 mm
Bushings	Ø28 / Ø18 × 22 mm
Axial end float	0.5 mm shown at right

Shell and bushings rotate about the fixed shaft.

Corner apartment

TWO-BEDROOM PLAN / DAYLIGHT, CENTRAL SERVICE CORE AND OPENING SCHEDULE

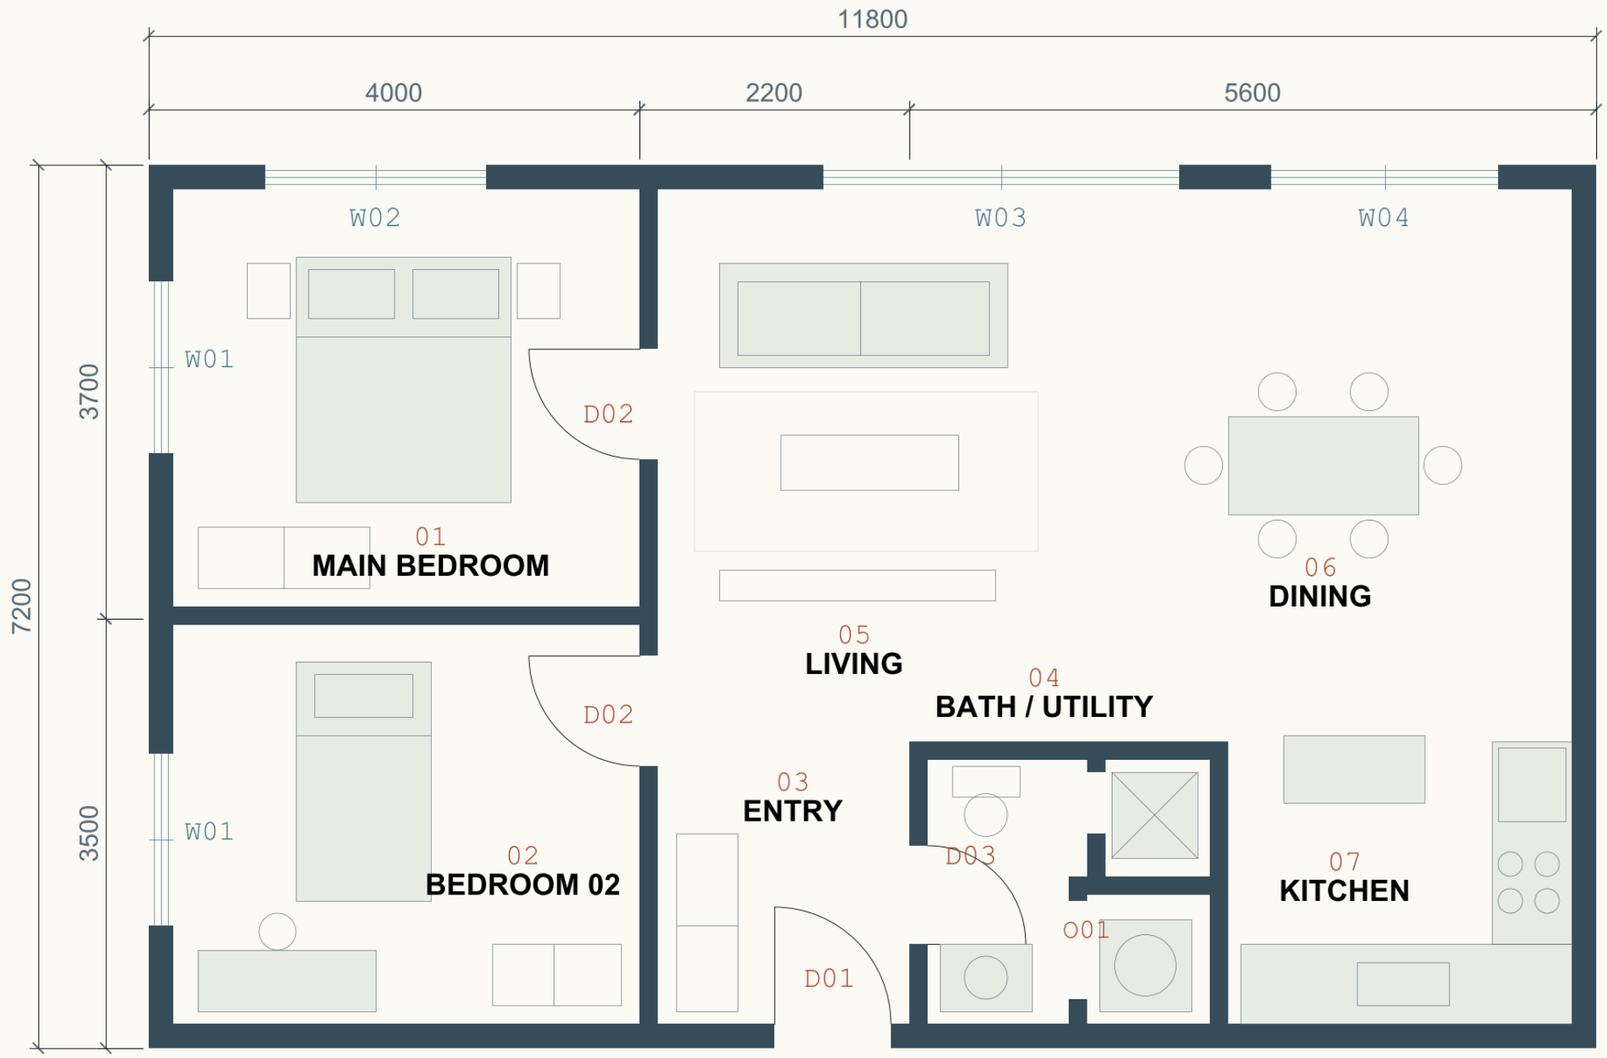

01 FURNISHED PLAN

OPENING SCHEDULE

ID	W (MM)	QTY	TYPE
D01	950	1	Entry swing
D02	900	2	Bedroom swing
D03	800	1	Bath swing
O01	800	1	Utility opening
W01	1400	2	West window
W02	1800	1	North window
W03	2900	1	North glazing
W04	1850	1	North window

GROSS FOOTPRINT

84.96 m²


11.80 × 7.20 m outside face.
Bedrooms share the west edge.
Bath, shower and laundry cluster beside the kitchen.

N

0 1 2 3 m

Relay start / stop control

24 V DC LADDER / SEAL-IN CONTACT, COIL SUPPRESSION AND TWO STATUS OUTPUTS

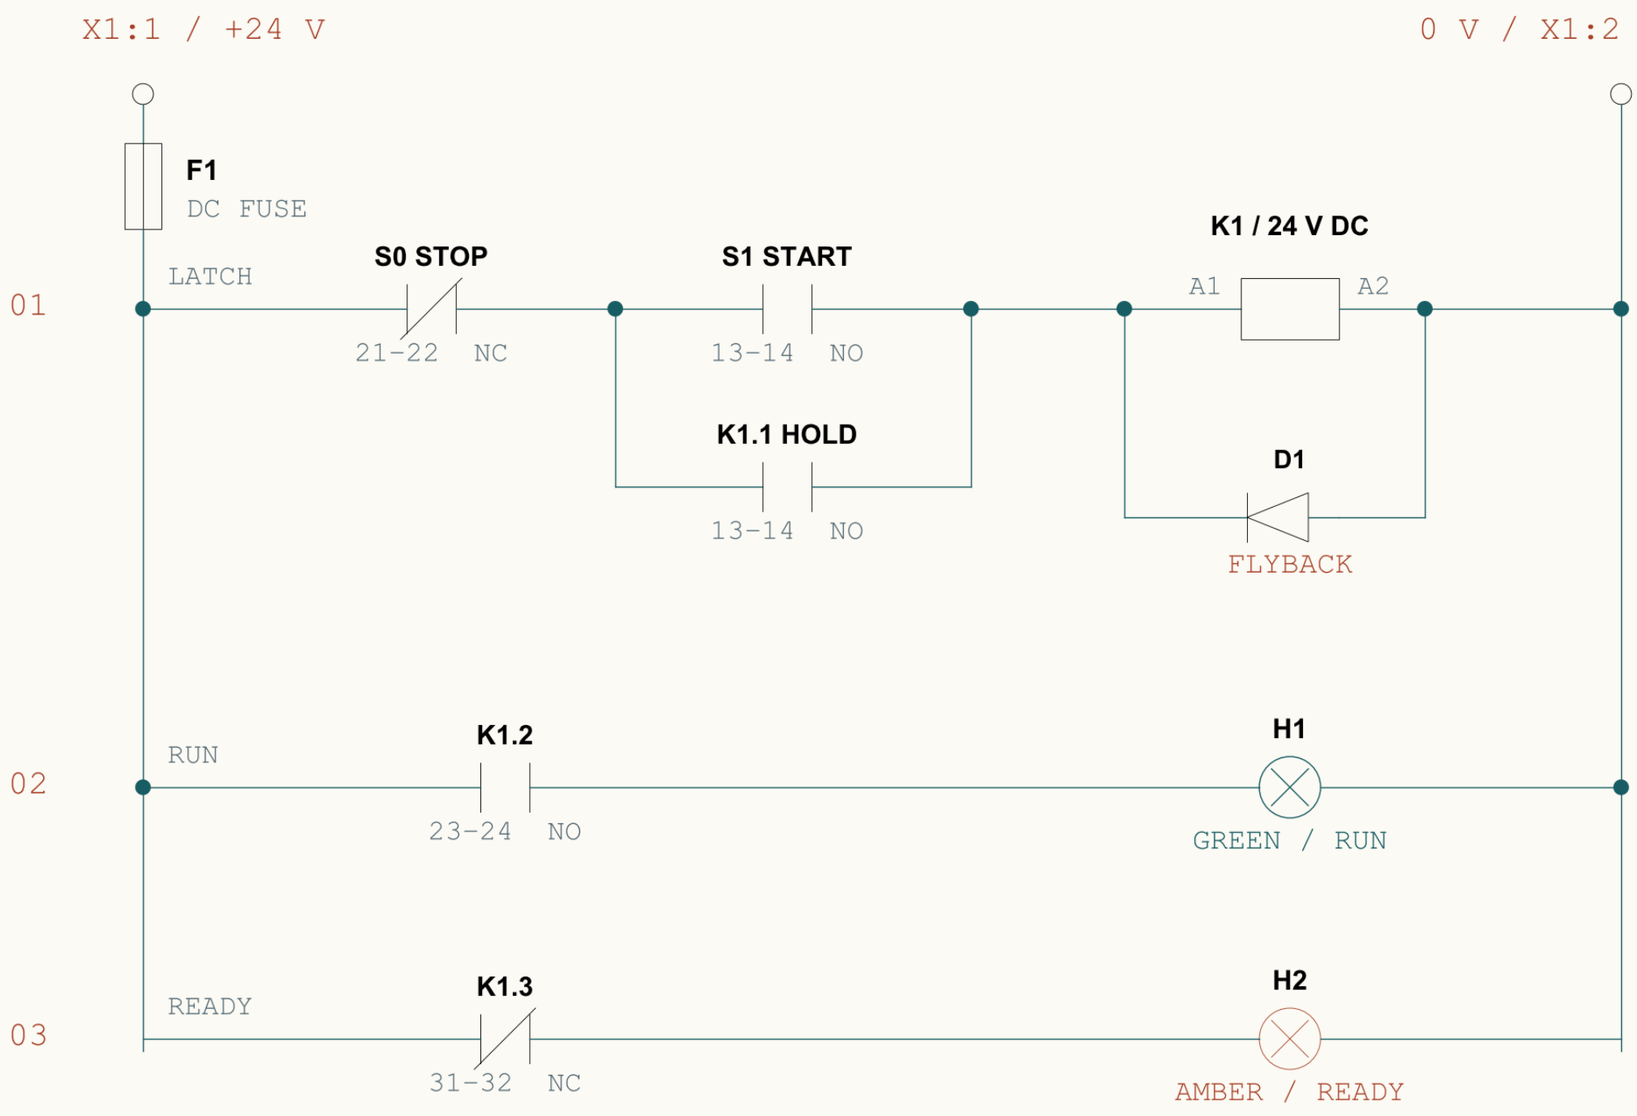

STATE TABLE / POWER ON

ACTION	K1	RUN	READY
At rest	OFF	OFF	ON
Tap START	ON	ON	OFF
Release START	ON	ON	OFF
Press STOP	OFF	OFF	ON

K1 CONTACT MAP

REF	RUNG	FUNCTION
K1.1	01	Seal-in / NO
K1.2	02	RUN lamp / NO
K1.3	03	READY lamp / NC

COIL PROTECTION

D1 cathode at A1 (+).
On power loss K1 drops out.
With START released, K1 stays off when supply returns.